F:\PROJECT\7. MTR - SUMMARECON SERPONG APARTMENT\2. STR\1. FOR TENDER\MTR-1021_A1.dwg, 21/11/2014 17:14:56, PDFCreator, J~Ko

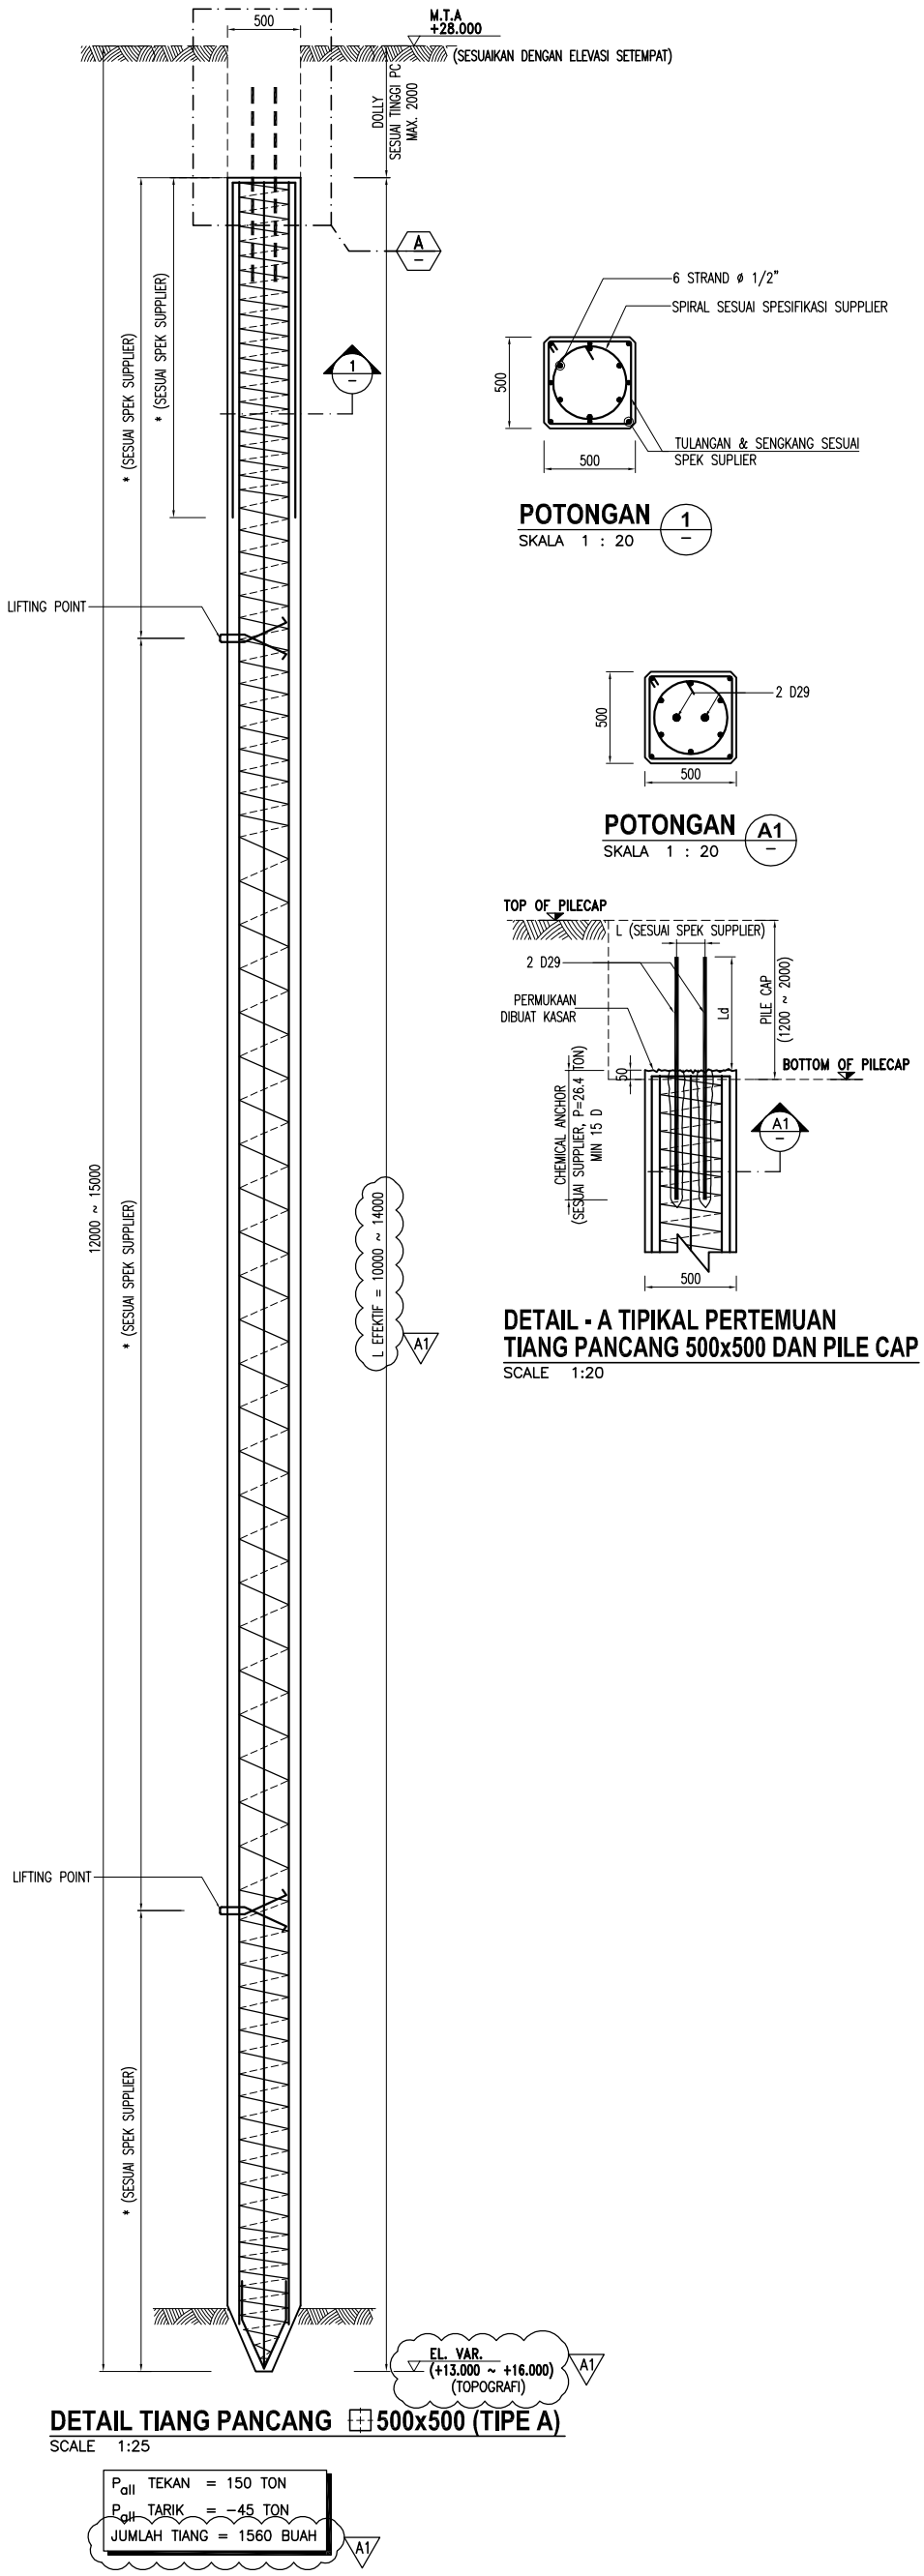

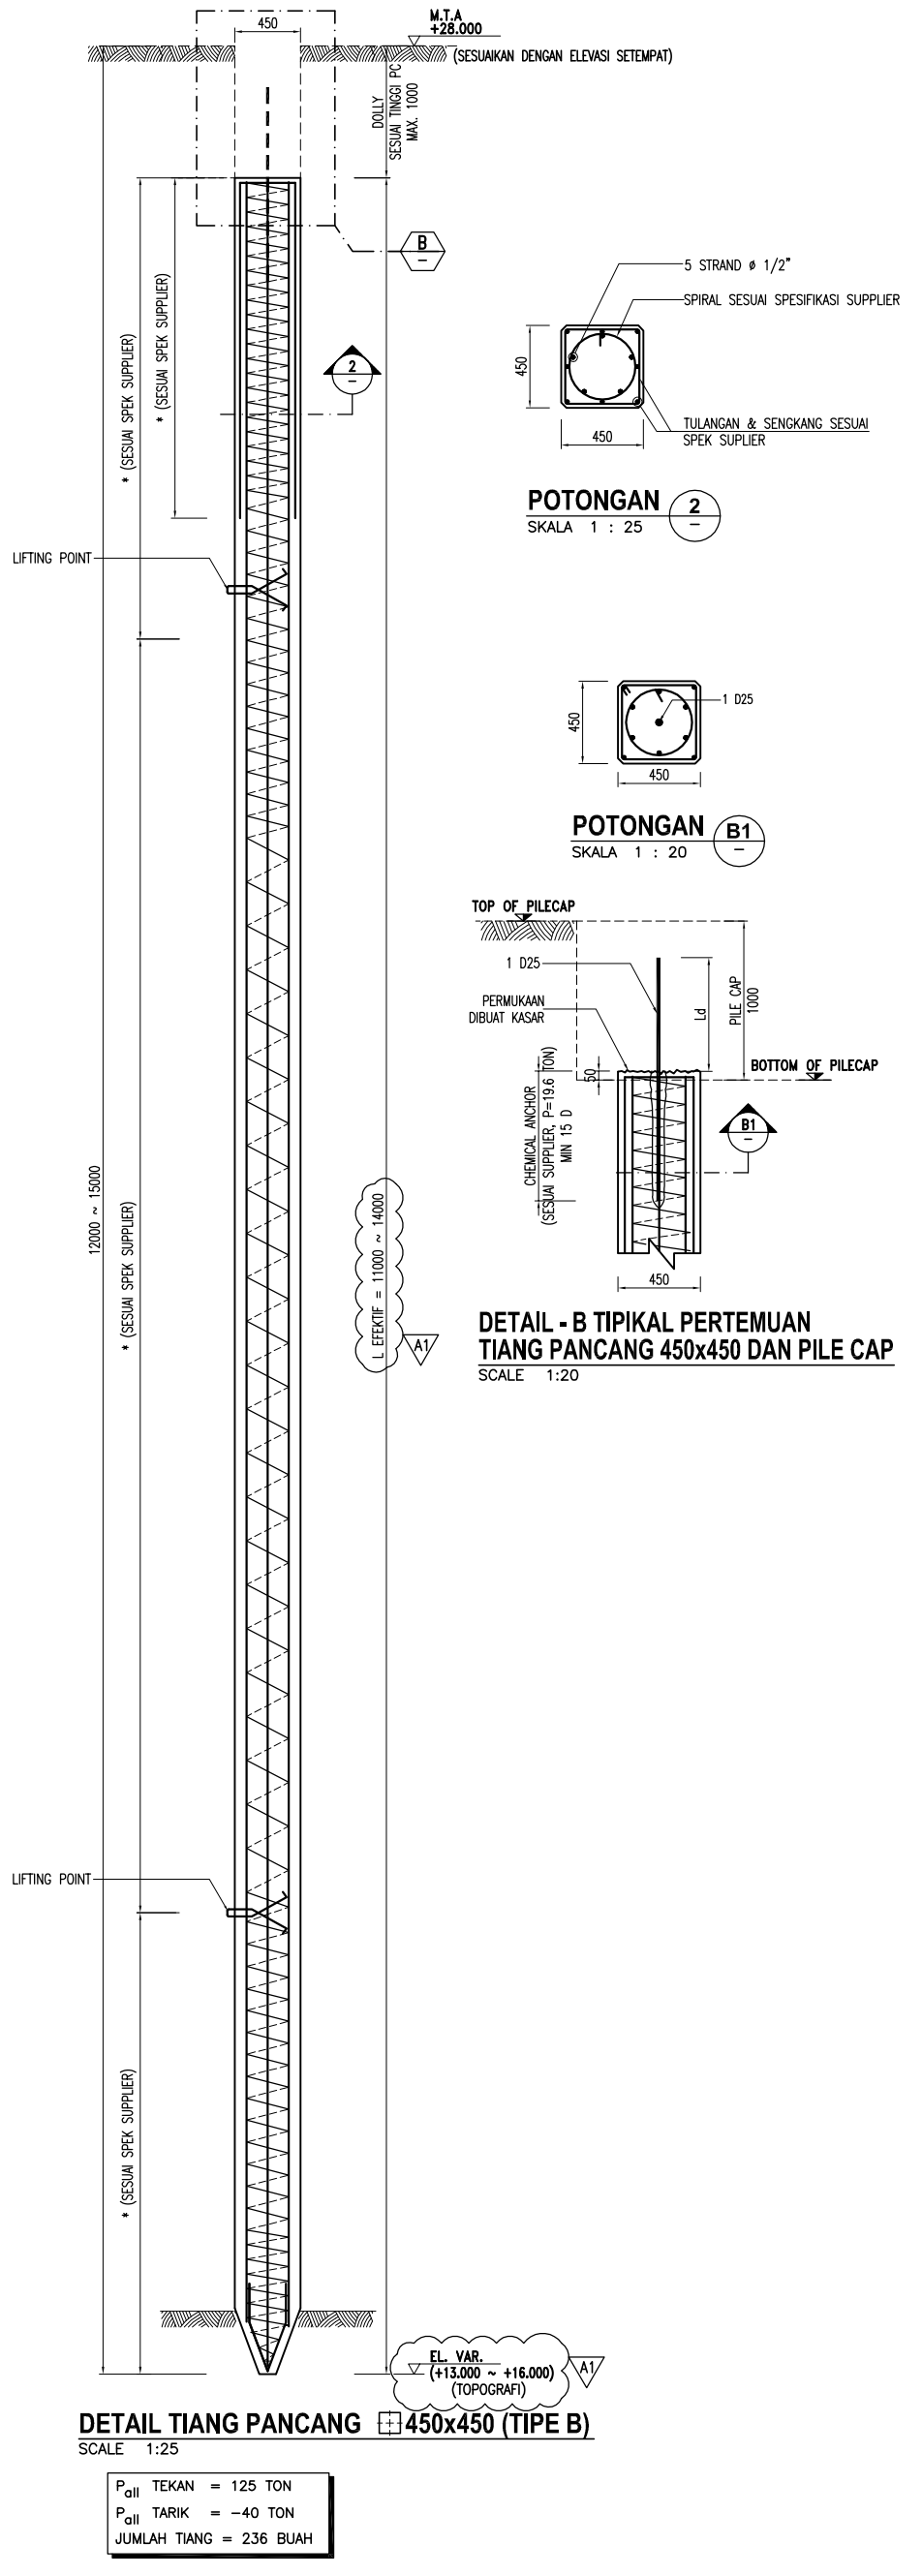

HAK CIPTA
DILARANG MENIRU ATAU MEREPRODUKSI GAMBAR INI DALAM BENTUK APAPUN JUGA, KECUALI DENGAN PERSETUJUAN TERTULIS DARI PT. DAVY SUKAMTA KONSULTAN

Keterangan
Notes

MUTU BAHAN

A. BETON
- TIANG PANCANG : K-500
- PELAT BASEMENT : UHAT S-0201
- KOLOM & SHEARWALL : UHAT S-0201
- PELAT & BALOK : UHAT S-0201

B. BESI TULANGAN
- ULIR (D)
  - a. D10 & D13 : F_y = 5000 Kg/cm2
  - b. > D13 : F_y = 4000 Kg/cm2
- POLOS (ø) : F_y = 3000 Kg/cm2

(KECUALI UTK PELAT BASEMENT, PILECAP & MAT)
- KHUSUS UNTUK PELAT BASEMENT, PILECAP & MAT FOUNDATION ULIR : F_y = 5000 Kg/cm2

NO	REVISION	DATE	SIGN.
A1	REVISI PANJANG & JUMLAH TP	21.11.14	
A0	FOR INFORMATION	02.06.14	

Proyek
Project

SERPONG MIDTOWN RESIDENCE

Pemberi Tugas
Owner

summarecon
Wonderful Life Wonderful World

PT KSO SUMMARECON SERPONG

Konsultan Arsitek/Lokal
Architect Consultant

P.T. ARMAS ASRI
ARCHITECTS+ ENGINEERS + CONSULTANTS
Jl. Cikini Raya No. 6 Jakarta 10330 Indonesia
Phone 31906888 Fax. 31906787

Konsultan Fasad
Facade Consultant

Konsultan Struktur
Structur Consultant

PT. DAVY SUKAMTA KONSULTAN
STRUCTURAL ENGINEER
Pondok Pinang Centre Blok A/18,
Jl. Cipulan Raya, Jakarta 12310 Tel.: 002-021-7511523
Facsimile 002-021-7511525, E-mail: sukamta@ipi.net.id

PENANGGUNG JAWAB PERENCANA STRUKTUR :
S I P T B
NAMA : Ir. Davy Sukamta
NO. : 0165/P/K-A/DPPB/**XII**-2012

PENANGGUNG JAWAB GEOTEKNIK :
S I P T B
NAMA : Stephen Gunawan Handoko, MT.
NO. : 0713/P/G-A/DPPB/**II**-2011

Konsultan M & E
M & E Consultant

PT. SIGMATECH TATAKARSA
MECHANICAL & ELECTRICAL ENGINEERS
Jl. Pangeran Jayakarta No. 17 Jakarta 10730
Ph.: (021) 7919 0904 – 7919 0905, Fax.: 7919 0707
E-mail: mail@sigmatech.co.id
Website: www.sigmatech.co.id
Certified for Quality Management System in ISO 9001:2008

Konsultan Landscape
Landscape Consultant

T O W N L A N D
Graha Aktiva, Lantai 7 Tower Utara
Jl. H.R. Rasuna Said Blok C-22, Jakarta 12940 - INDONESIA
Tel. +62 21 2941 0001, Fax. +62 21 2941 0002 (www.townland.com)

Konsultan Lighting
Lighting Consultant

Quantity Surveyor

Judul gambar
Drawing Title

DETAIL TIANG PANCANG

	NAME	SIGN
CONSULTANT		
Drawn By	J~KO	
Project Manager	Ir. JAMES F. KULIT	
Project Director	Ir. DAVY SUKAMTA	
OWNER		
Design Engineer		
Design Koordinator		
SCALE	1 : 25 ; 20	
ISSUED FOR	REVISION	DRAWING CODE/NO
FOR INFORMATION	A1	S-1021
Tanggal 21.11.2014	No.File/Date/OPR	
Project Code		
Owner DSS		
Consultant 286a		