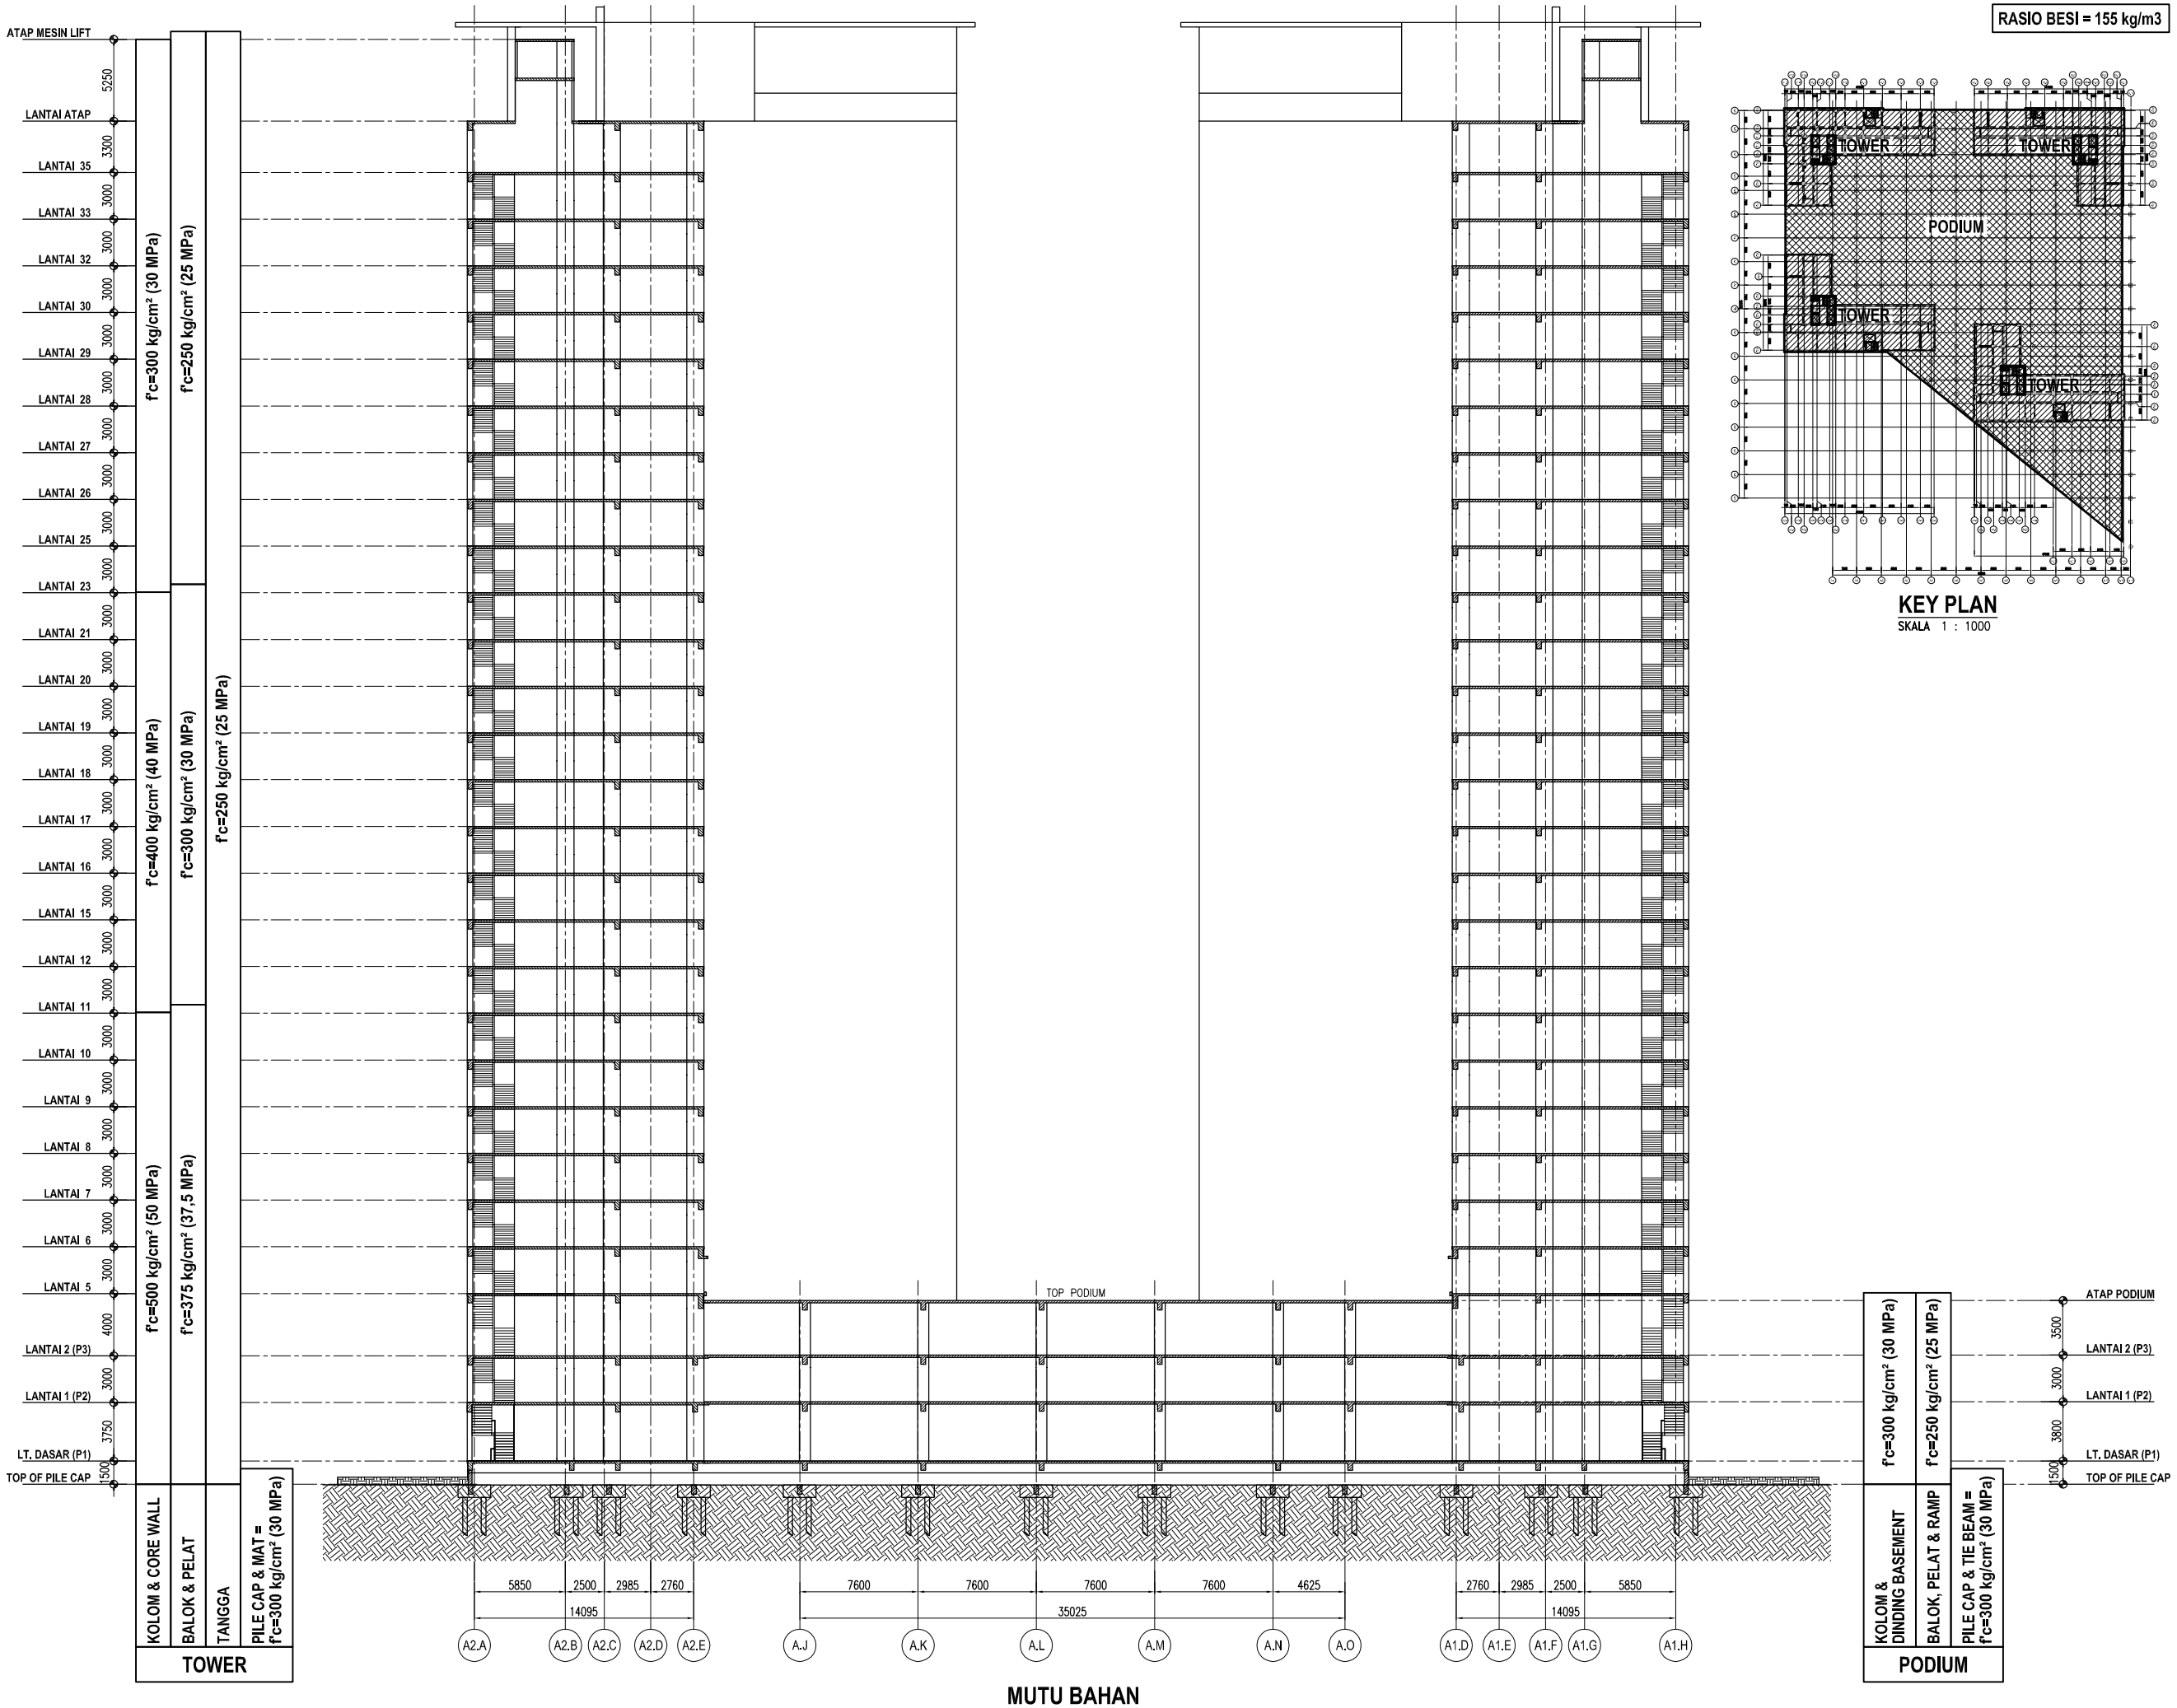

MUTU BAHAN
SKALA 1:200

RASIO BESI = 155 kg/m3

KEY PLAN
SKALA 1 : 1000

HAK CIPTA
DILARANG MENIRU ATAU MEREPRODUKSI GAMBAR INI DALAM BENTUK APAPUN JUGA , KECUALI DENGAN PERSETUJUAN TERTULIS DARI PT. DAVY SUKAMTA KONSULTAN

Keterangan
Notes

MUTU BAHAN

A. BETON
- TIANG PANCANG : K-500
- PELAT BASEMENT : LIHAT S-0201
- KOLOM & SHEARWALL : LIHAT S-0201
- PELAT & BALOK : LIHAT S-0201

B. BESI TULANGAN
- UUR (D)
  - a. D10 & D13 : Fy = 5000 Kg/cm2
  - b. > D13 : Fy = 4000 Kg/cm2
  - (KECUALI UTK PELAT BASEMENT, PILECAP & MAT)
- POLOS (ø) : Fy = 3000 Kg/cm2
- KHUSUS UNTUK PELAT BASEMENT, PILECAP & MAT FOUNDATION, UUR : Fy = 5000 Kg/cm2

NO	REVISION	DATE	SIGN.
A0	FOR INFORMATION	21.11.14	

Proyek
Project

SERPONG
MIDTOWN RESIDENCE

Pemberi Tugas
Owner

summarecon
Wonderful Life Wonderful World

PT KSO SUMMARECON SERPONG

Konsultan Arsitek/Lokal
Architect Consultant

P.T. AIRMAS ASRI
ARCHITECTS • ENGINEERS • CONSULTANTS
Jl. Cikini IV No. 6 Jakarta 10330 Indonesia
Phone 31906688 Fax. 31906767

Konsultan Fasad
Facade Consultant

Konsultan Struktur
Structur Consultant

PT. DAVY SUKAMTA KONSULTAN
STRUCTURAL ENGINEER
Pondok Pinang Centre Blok A/18,
Jl. Cipulat Raya, Jakarta 12310 Telp. 062-021- 7511523
Facsimile 062-021- 7511525, E-mail : sukamta@ad.net.id

PENANGGUNG JAWAB PERENCANA STRUKTUR :
SIPTB
NAMA : Ir. Davy Sukamta
NO. : 0165/P/K-A/DPPB/XIII-2012

PENANGGUNG JAWAB GEOTEKNIK :
SIPTB
NAMA : Stephen Gunawan Handoko, MT.
NO. : 0713/P/G-A/DPPB/II-2011

Konsultan M & E
M & E Consultant

PT. SIGMATECH TATAKARSA
MECHANICAL & ELECTRICAL ENGINEERS
Jl. Pengadegan Utara No.16, Jakarta 12770
Ph.: (021) 7919 0954 – 7919 0955, Fax.: 7919 5787
E-mail : mail@sigmatech.co.id
Website : www.sigmatech.co.id
Certified for Quality Management System in ISO 9001:2008

Quantity Surveyor

Konsultan Lighting
Lighting Consultant

Konsultan Landscape
Landscape Consultant

TOWNLAND
Granadi Building, Lantai 7 Tajdid Utara
Jl. H.R. Rasuna Said Blok X-1 Kav. 5-6, Kuningan, Jakarta Selatan – 12950, Indonesia
Tel: +62 21 2941 0621, Fax: +62 21 2941 0622 (www.townland.com)

Judul gambar
Drawing Title

MUTU BAHAN

CONSULTANT	NAME	SIGN
Drawn By	J~KO	
Project Manager	Ir. JAMES F. KULLIT	
Project Director	Ir. DAVY SUKAMTA	
OWNER		
Design Engineer		
Design Koordinator		
SCALE	1 : 200	

ISSUED FOR		REVISION	DRAWING CODE/NO
FOR INFORMATION		A0	S-0201
Tanggal	21.11.2014		
Project Code		No.File/Date/OPR	
Owner	DSS		
Consultant	286a		

F:\PROJECT\7. MTR - SUMMARECON SERPONG APARTMENT\2. STR\1. FOR TENDER\MTR-0201_A0.dwg, 21/11/2014 17:16:45, PDFCreator, J~Ko